

Freiflächenplan	Maßstab: 1:500	Beb.-Plan:		Zul. Geschosse:
	GRZ:	GFZ:	BMZ:	Dachart u. Dachn.:

Stadt: Ahlen
Gemeinde: Ahlen
Gemarkung: Ahlen

Flur 26

Flst.	Fläche	Grb.	Eigentümer
168	ca. 22		DITIB Ahlen – ULU CAMI Rottmannstr. 62, 59229 Ahlen
170	ca. 15		DITIB Ahlen – ULU CAMI Rottmannstr. 62, 59229 Ahlen
172	ca. 654		DITIB Ahlen – ULU CAMI Rottmannstr. 62, 59229 Ahlen
177	ca. 575		DITIB Ahlen – ULU CAMI Rottmannstr. 62, 59229 Ahlen
330	ca. 297		DITIB Ahlen – ULU CAMI Rottmannstr. 62, 59229 Ahlen
681	ca. 851		DITIB Ahlen – ULU CAMI Rottmannstr. 62, 59229 Ahlen
799	ca. 699		DITIB Ahlen – ULU CAMI Rottmannstr. 62, 59229 Ahlen
Gesamt	ca. 3.113		

Datum: 06.10.2025

Bauherr:
DITIB Ahlen – ULU CAMI
i. V. Herr Ali Koça, Mustafa Terken
Rottmannstr. 62, 59229 Ahlen

Unterschrift Bauherr


Bauvorhaben:
Errichtung einer Begegnungs- und
Kulturstätte mit Büro und
Verwaltung
Rottmannstr. 62, 59229 Ahlen

Entwurfsverfasser:
Dipl. – Ing. Bernd Theismann
Nordstr. 29
59227 Ahlen



Ämliche Eintragungen

Legende:	
	öffentl. Verkehrsfläche
	private Verkehrsfläche/Stellplatz
	Neu (Hauptgebäude)
	Neu (Nebengebäude)
	Dachbegrünung
	besteh. Gebäude
	Grünfläche
	Abstandsfläche
	Flurstücksnummer
	Feuerwehraufstellfläche
	Abbruch
	Stellplatz
	Spielfeld
	Baulast
	Lade- & Leitungsinfrastruktur (E-Mobil.)
	F = Fahrradabstellfläche M = Mülltonnen

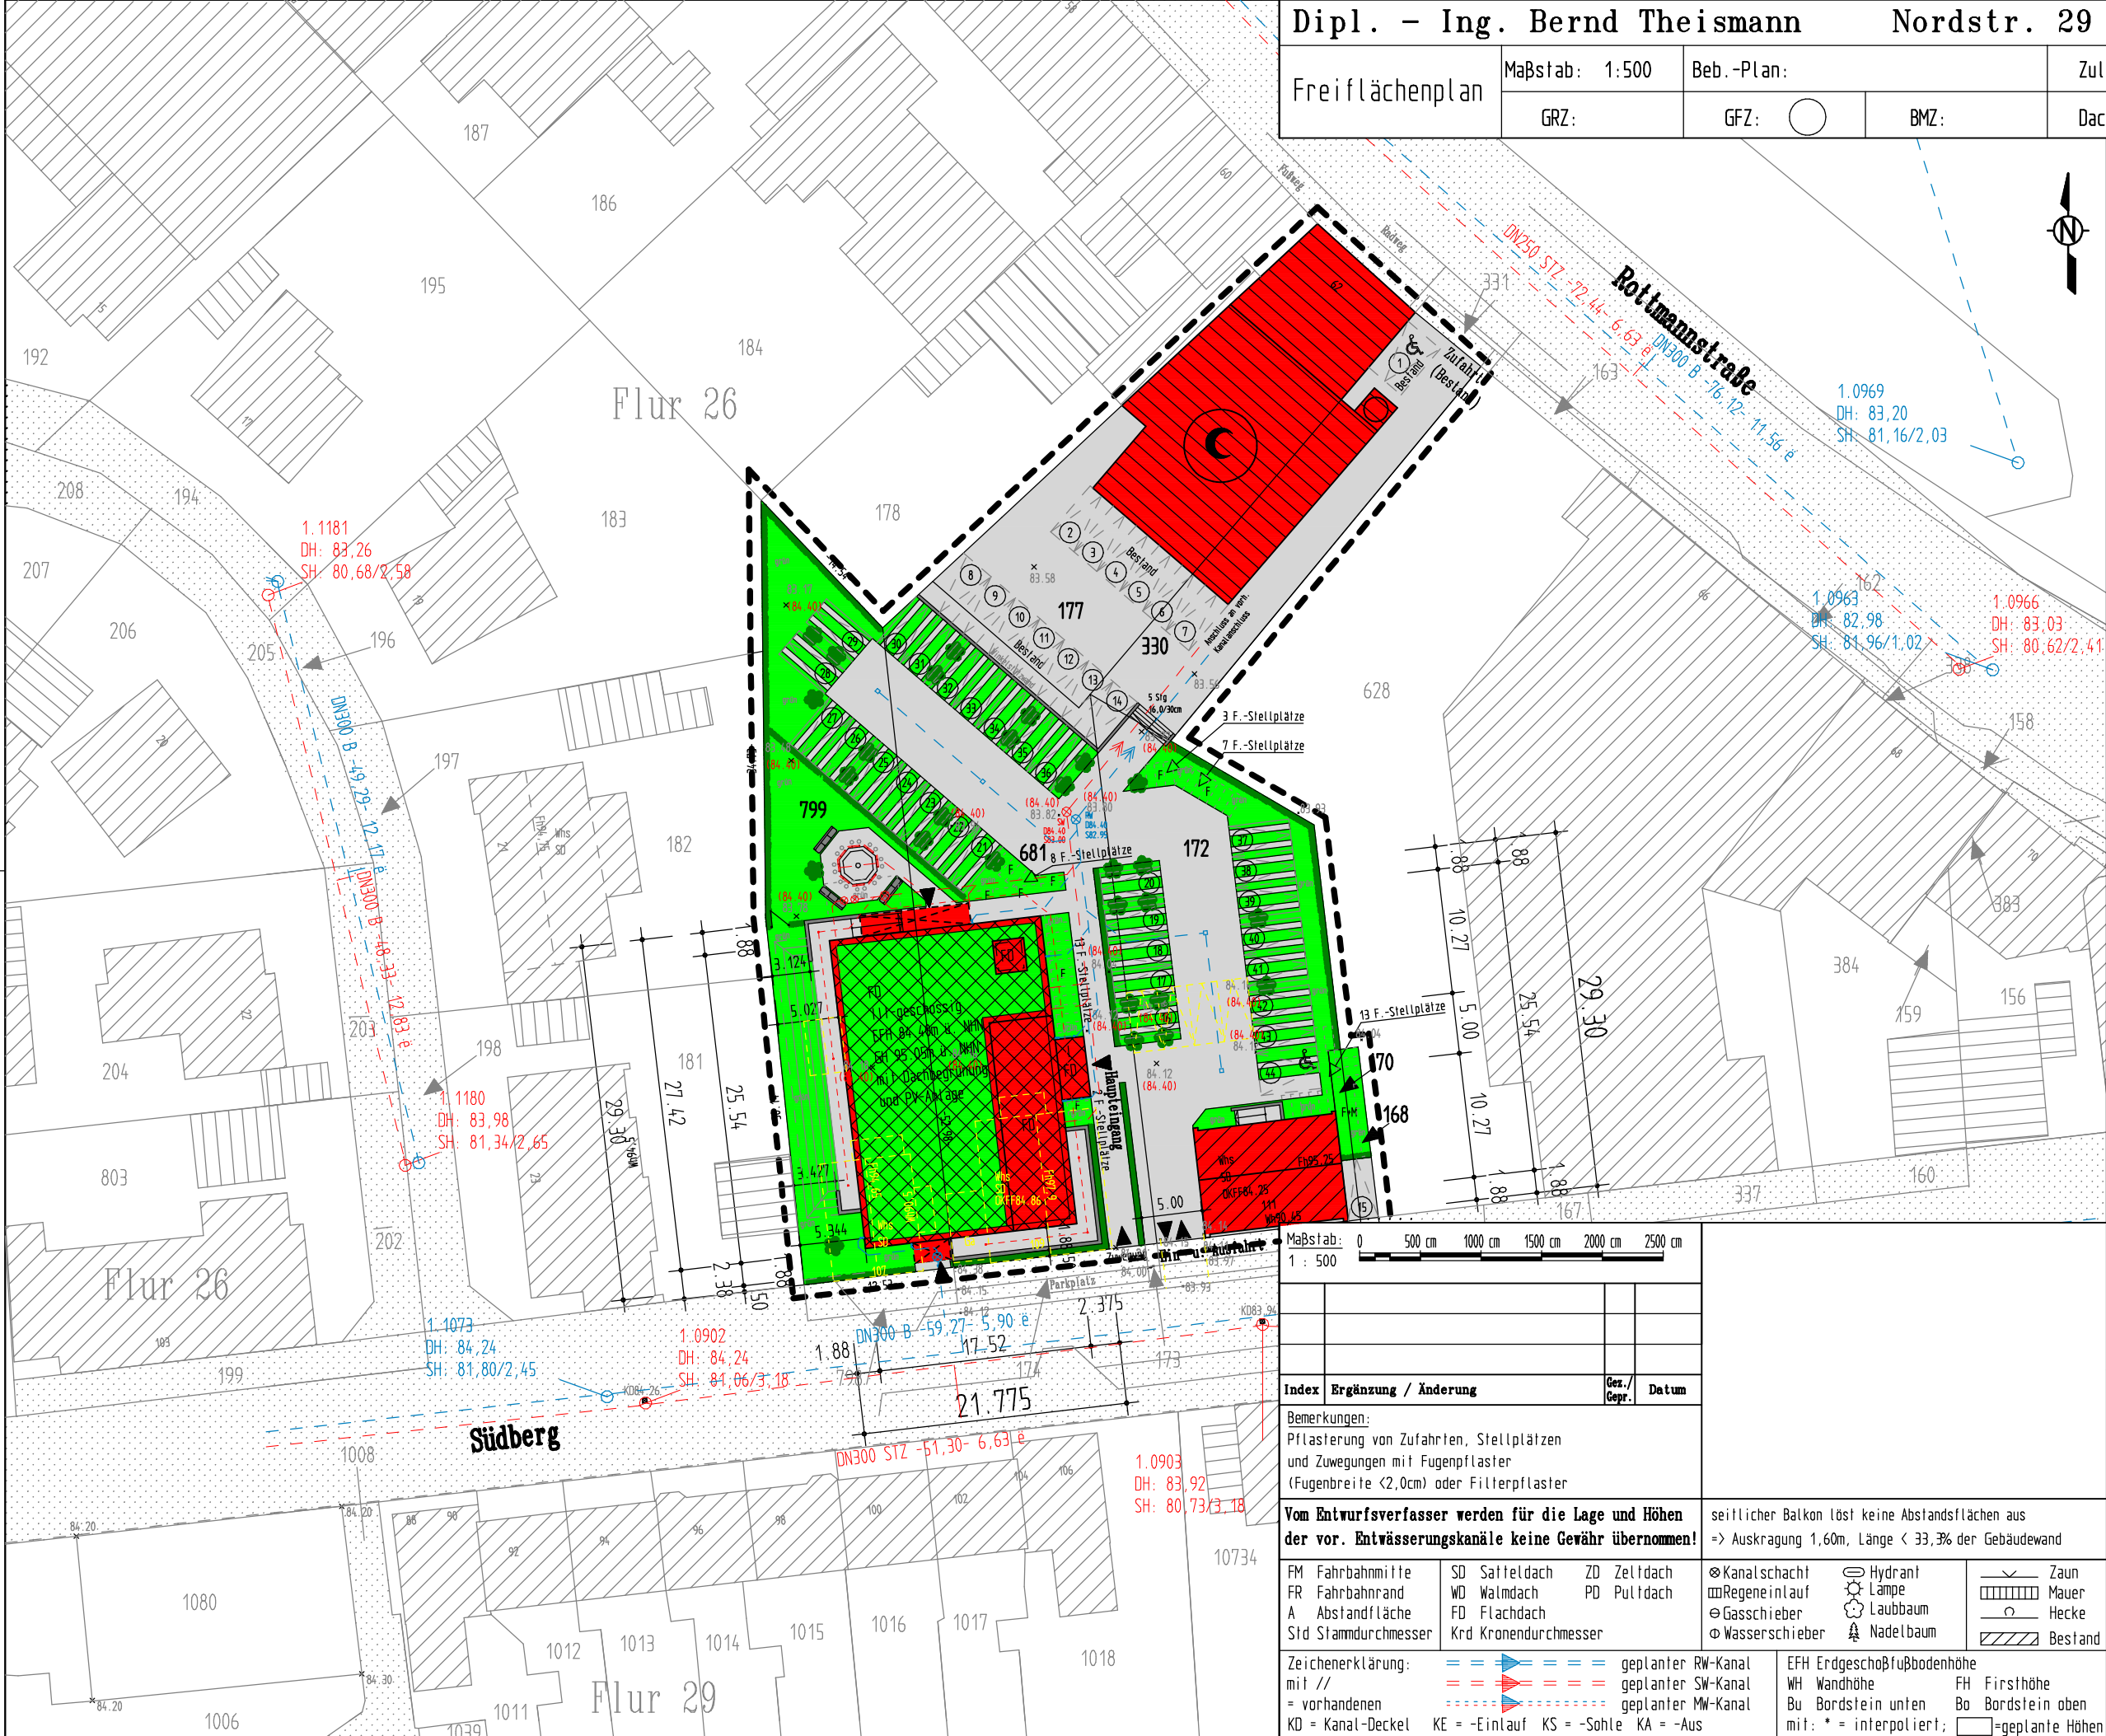

Maßstab: 1 : 500

Index	Ergänzung / Änderung	Ges./Gepr.	Datum
-------	----------------------	------------	-------

Bemerkungen:
Pflasterung von Zufahrten, Stellplätzen
und Zuwegungen mit Fugenpflaster
(Fugenbreite <2,0cm) oder Filterpflaster

Vom Entwurfsverfasser werden für die Lage und Höhen
der vor. Entwässerungskanäle keine Gewähr übernommen!

FM	Fahrbahnmitte	SD	Satteldach	ZD	Zeltdach
FR	Fahrbahnrand	WD	Walmdach	PD	Pultdach
A	Abstandsfläche	FD	Flachdach		
Std	Stammdurchmesser	Krd	Kronendurchmesser		

Zeichenerklärung:
mit // = vorhandenen
geplanter RW-Kanal
geplanter SW-Kanal
geplanter MW-Kanal
KD = Kanal-Deckel
KE = -Einlauf
KS = -Sohle
KA = -Aus

	Kanalschacht		Hydrant		Zaun
	Regeneinlauf		Lampe		Mauer
	Gasschieber		Laubbaum		Hecke
	Wasserschieber		Nadelbaum		Bestand

EFH Erdgeschoßfußbodenhöhe
WH Wandhöhe
Bu Bordstein unten
mit: * = interpoliert;
FH Firsthöhe
Bo Bordstein oben
= geplante Höhen