

Hinweis Barrierefreiheit:  
Das Barrierefrei-Konzept durch das Ingenieurbüro Theismann und Partner,  
Dipl.-Ing. Bernd Theismann, ist zu beachten und umzusetzen!  
(Nordstraße 29, 59227 Ahlen)

bauaufsichtliche Sichtvermerke:

- Legende
- VMZ 20-2,0/MG III
  - Mauerwerk (Neu) PP 2-0,35/Db
  - Mauerwerk (Neu) KS 12-1,4/MG IIa
  - Mauerwerk (Neu) KS 20-2,2/MG IIa
  - Stahlbeton (Neu)
  - Trockenbau (Neu)
  - Bestand
  - Neu
  - Brettsperrholzelemente
  - Abbruch
  - Lade- & Leitungsinfrastruktur (E-Mobilität)
  - rollstuhlgerechte Whg. (gem. DIN 18040-2:2011-09)

Maßstab 1:100 0 100 cm 200 cm 300 cm 400 cm 500 cm

| Index | Ergänzung / Änderung | Ges./<br>Gepr. | Datum |
|-------|----------------------|----------------|-------|
|       |                      |                |       |
|       |                      |                |       |

DIESE ZEICHNUNG GILT NUR IN VERBINDUNG MIT DEN STATISCHEN UNTERLAGEN !  
ALLE MAßE SIND AM BAU ZU PRÜFEN UND MIT DER BAULEITUNG ABZUSTIMMEN !  
DIE ALLEINIGEN VEREHRERRECHTE LIEGEN BEIM ENTWURFSVERFASSER !

Entwurfsverfasser:  
**Dipl. - Ing. Bernd Theismann**  
Ingenieurbüro für Baukonstruktion  
Nordstraße 29 • 59227 Ahlen  
Fon 02382/85050 Fax 02382/85051  
info@theismannundpartner.de


BAUHERR :  
DITIB Ahlen - ULU CAMI  
i. V. Herr Ali Koca und Mustafa Terken  
Rottmannstr. 62  
59229 Ahlen

BAUVORHABEN :  
Errichtung einer Begegnungs- und Kulturstätte  
mit Büro und Verwaltung  
Rottmannstr. 62, 59229 Ahlen 168/170/177/330/  
Gemarkung Ahlen, Flur 26, Flurstück/e 681/799

Ansichten

DATUM : 06.10.2025  
MAßSTAB : 1 : 100  
AUFTR - Nr. : 274001  
BLATT - Nr. : GEO2

Ingenieurkammer-Bau  
Nordrhein-Westfalen  
Mitglied der Kammer  
Dipl.-Ing. Bernd Theismann  
Bauverlag  
berechtigt  
Unterschrift Entwurfsverfasser

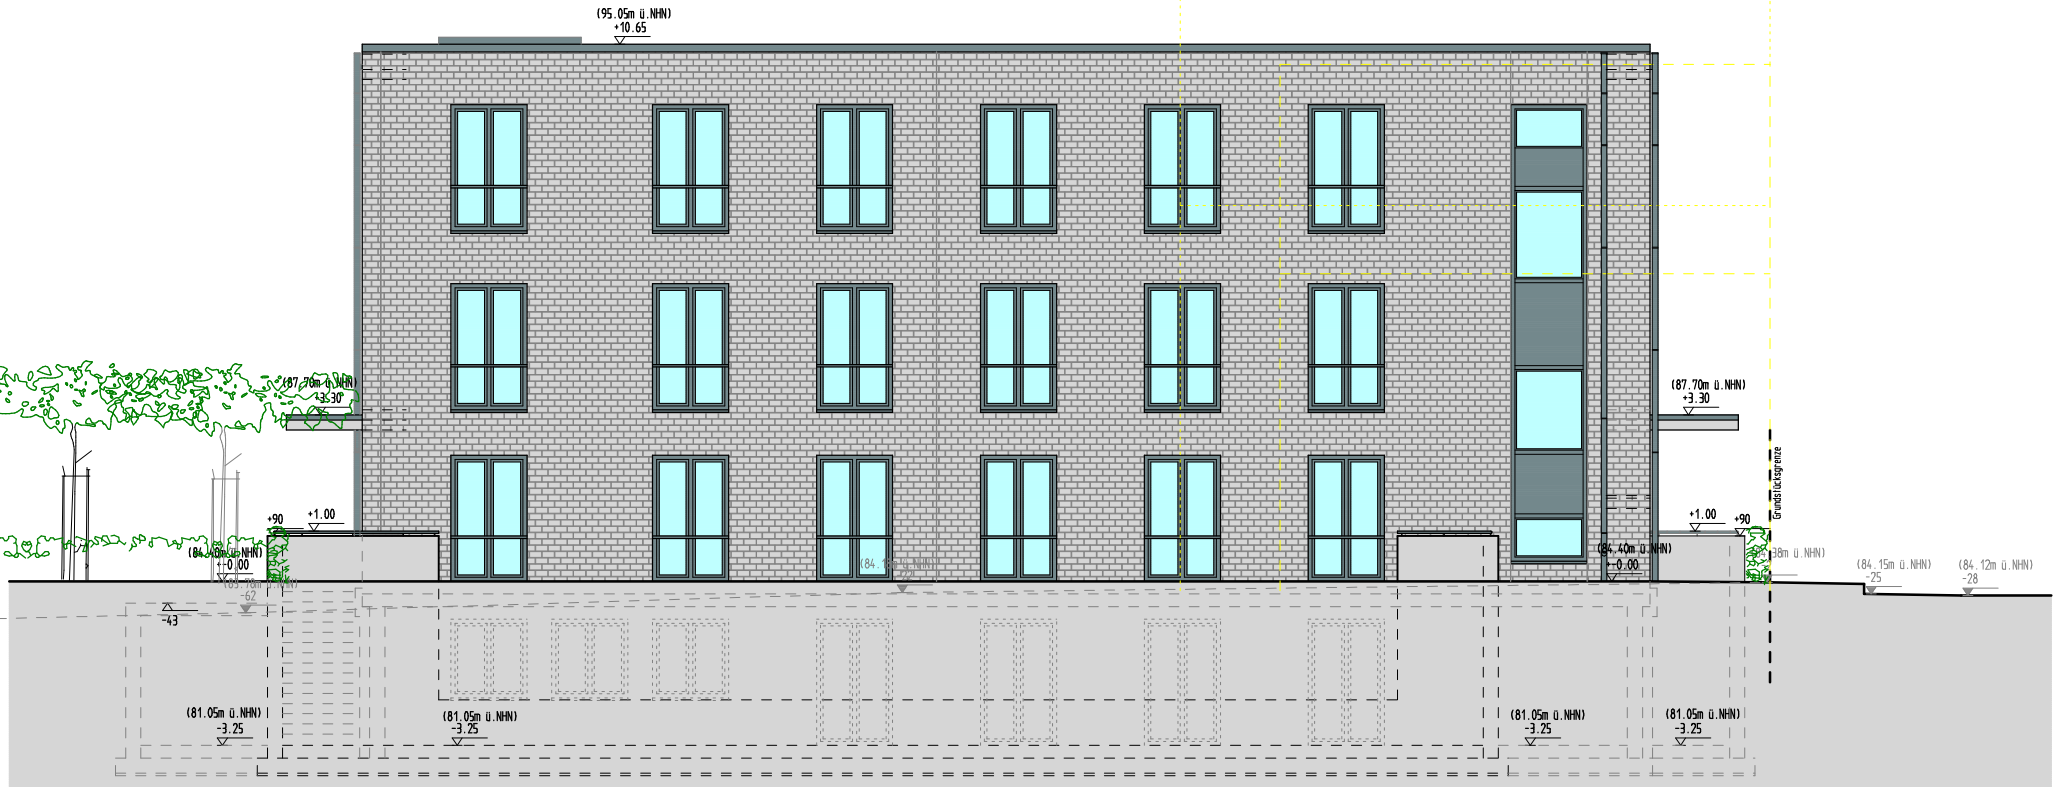

Westansicht

Westansicht



Südansicht (Südberg)

Südansicht (Südberg)

Hinweis:  
Das Brandschutzkonzept durch das Prüfingenieurbüro  
Genähr-Beratende Ingenieure PartG mbH ist zu beachten!  
(Stockholmer Allee 24, 44269 Dortmund)

Brandschutz:  
fh = feuerhemmend F30  
hf = hochfeuerhemmend F60  
fb = feuerbeständig F90  
nb = nicht brennbar  
BW = Brandwand  
WaBW = Wand anstelle einer Brandwand  
BBW = Bauart einer Brandwand  
T30, T60, T90 = Feuerwiderstandsklasse  
M = mechanische Beanspruchung  
RS = Rauchschutzabschluss (DIN18095)  
S = Selbstschließend  
D = Dichtschießend  
V = Vollwandig  
N = Nichtabsperren  
PS = Panikschloss

1. Rettungsweg  
2. Rettungsweg  
Notausstieg (2. RN)  
Tur-Öffnungsmaß (roh)  
Tur-Öffnungsmaß (fertig)  
Barrierefreiheit (Höhe von OKFFB)