


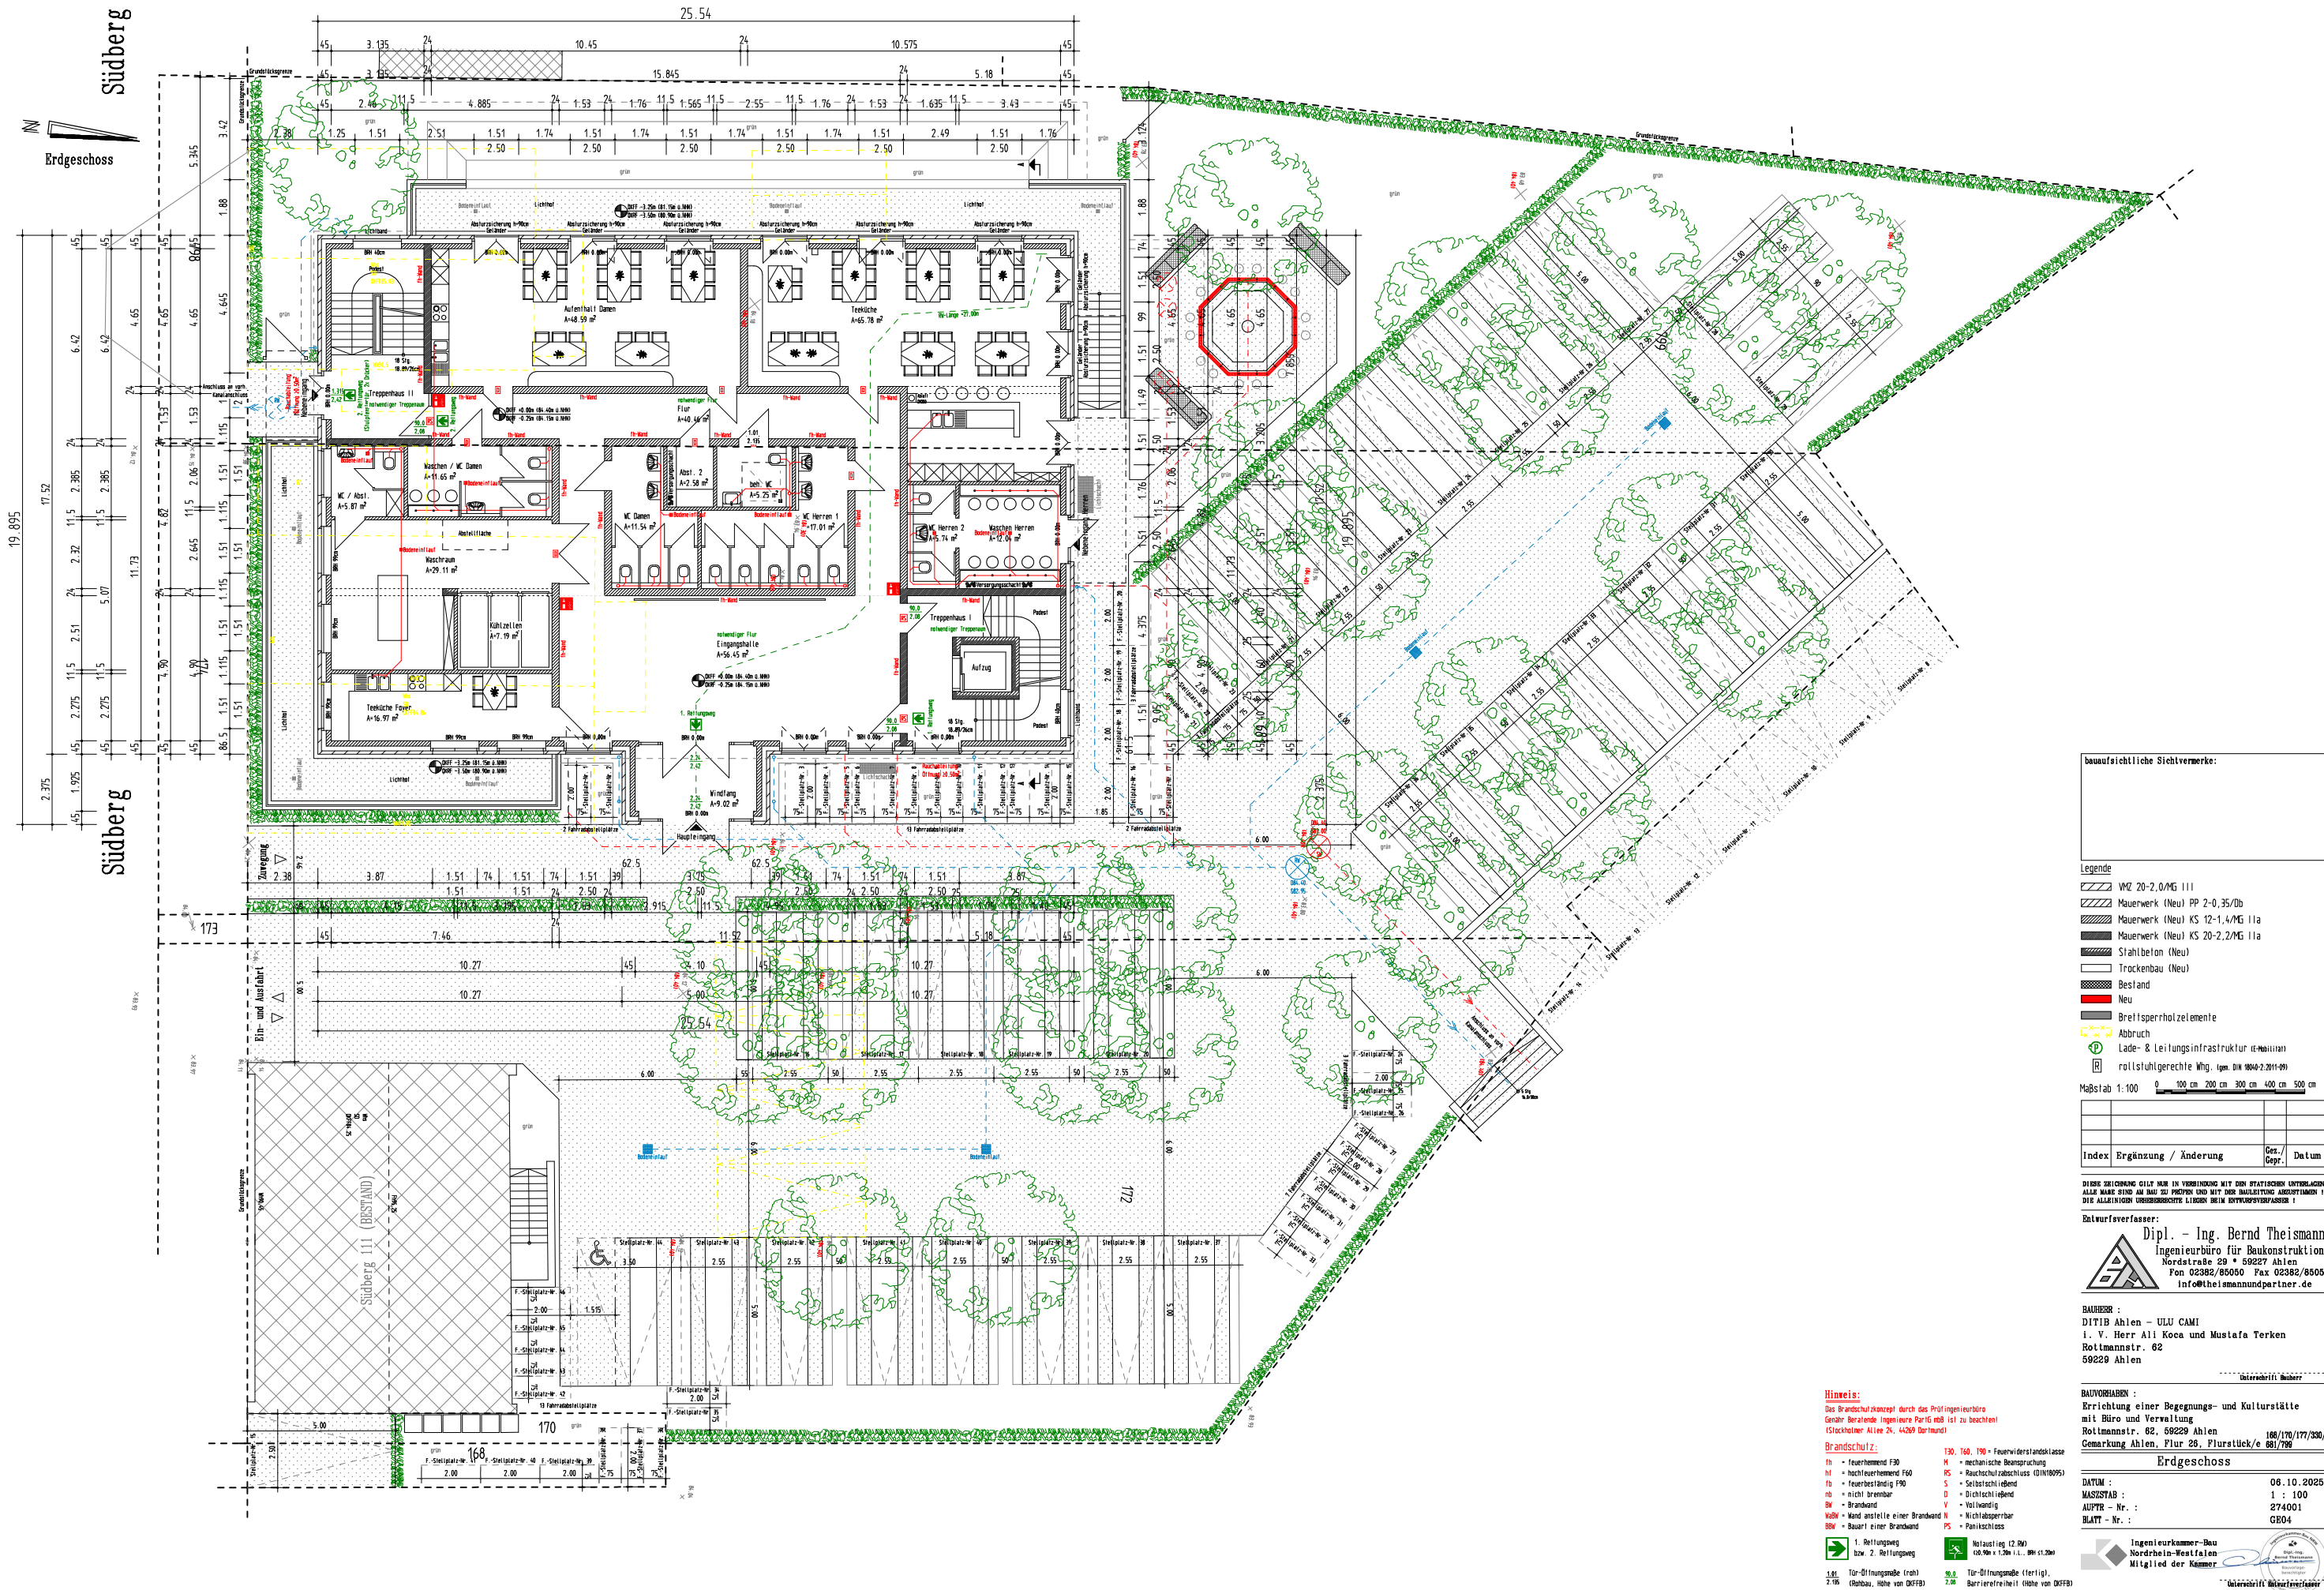

bauaufsichtliche Sichtvermerke:

- Legende
- WM 20-2,0/MG III
 - Mauerwerk (Neu) PP 2-0,35/Ob
 - Mauerwerk (Neu) KS 12-1,4/MG IIa
 - Mauerwerk (Neu) KS 20-2,2/MG IIa
 - Stahlbeton (Neu)
 - Trockenbau (Neu)
 - Bestand
 - Neu
 - Breitsperrholzelemente
 - Abbruch
 - Lade- & Leitungsinfrastruktur (e-Mobilität)
 - rollstuhlgerechte Whg. (gem. DIN 18064-2:2011-09)

Maßstab 1:100

Index	Ergänzung / Änderung	Gr./	Datum
		Gepr.	

DIESE ZEICHNUNG GILT NUR IN VERBINDUNG MIT DEN STATISCHEN UNTERLAGEN!
ALLE ANDEREN SIND AN DER 20. SEPTEMBER 2011 MIT DER BAULEISTUNG ABGESTIMMT!
DIE ALTERNATION UNTERSCHREIBT LIEGEN BEIM BAUFÜHRER/VERFASSER!

Bauführer/Verfasser:

Dipl. - Ing. Bernd Theissmann
Ingenieurbüro für Baukonstruktion
Nordstraße 29 • 59227 Ahlen
Fon 02382/85050 Fax 02382/85051
info@theissmannundpartner.de

BAUHER:
DITIB Ahlen - ULU CAMI
i. V. Herr Ali Koca und Mustafa Terken
Rottmannstr. 62
59229 Ahlen

BAUVERFAHREN:
Errichtung einer Begegnungs- und Kulturstätte
mit Büro und Verwaltung
Rottmannstr. 62, 59229 Ahlen
Gemarkung Ahlen, Flur 28, Flurstück/e 108/170/177/330/
80/790

Datum: 06.10.2025
MASSSTAB: 1 : 100
AUFTR - Nr.: 274001
BLATT - Nr.: GB04

Ingenieurkammer-Bau
Nordrhein-Westfalen
Mitglied der Kammer
Unterschrift Bauverfasser

- Hinweis:
Das Brandschutzkonzept durch das Ingenieurbüro
Gastel, Bardele, Ingenieure PartG mbH ist zu beachten!
(Strothmann-Allee 24, 42699 Dortmund)
- Brandschutz:
- fr = Feuerhemmend F30
 - hf = hochfeuerhemmend F60
 - frb = feuerbeständig F120
 - nb = nicht brennbar
 - bw = Brandwand
 - WdN = Wand anstelle einer Brandwand
 - BNW = Bauart einer Brandwand
 - 130, 160, 190 = Feuerwiderstandsklasse
 - H = mechanische Beanspruchung
 - KS = Rauchschuttschluss (DIN 18095)
 - S = Selbstschließend
 - D = Dichtschließend
 - V = Vollwandig
 - N = Nichtabsperrbar
 - PS = Panikschloß
 - 1. Rettungs- bzw. 2. Rettungs- gang
 - 1.81 = Tür-Öffnungsmaß (roh) (Gebäude, Höhe von OGFB)
 - 2.15 = Barrierefreiheit (Höhe von OGFB)
 - 1.81 = Tür-Öffnungsmaß (fertig)
 - 2.15 = Barrierefreiheit (Höhe von OGFB)