
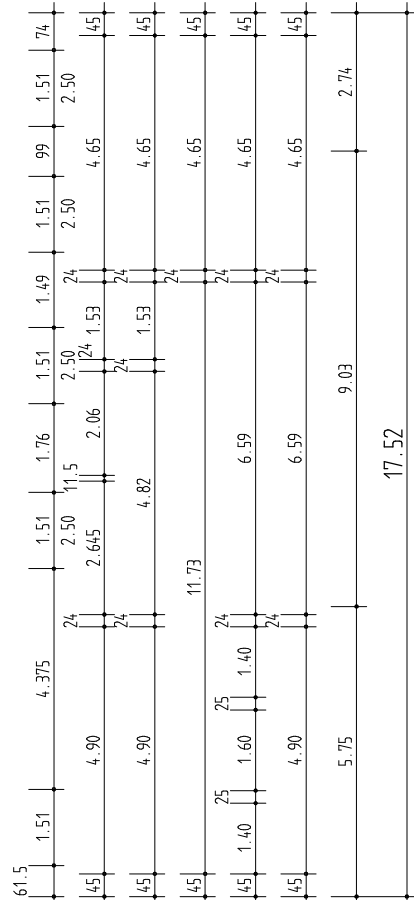


Hinweis Barrierefreiheit:
Das Barrierefrei-Konzept durch das Ingenieurbüro Theismann und Partner,
Dipl.-Ing. Bernd Theismann, ist zu beachten und umzusetzen!
(Nordstraße 29, 59227 Ahlen)

1. Obergeschoss

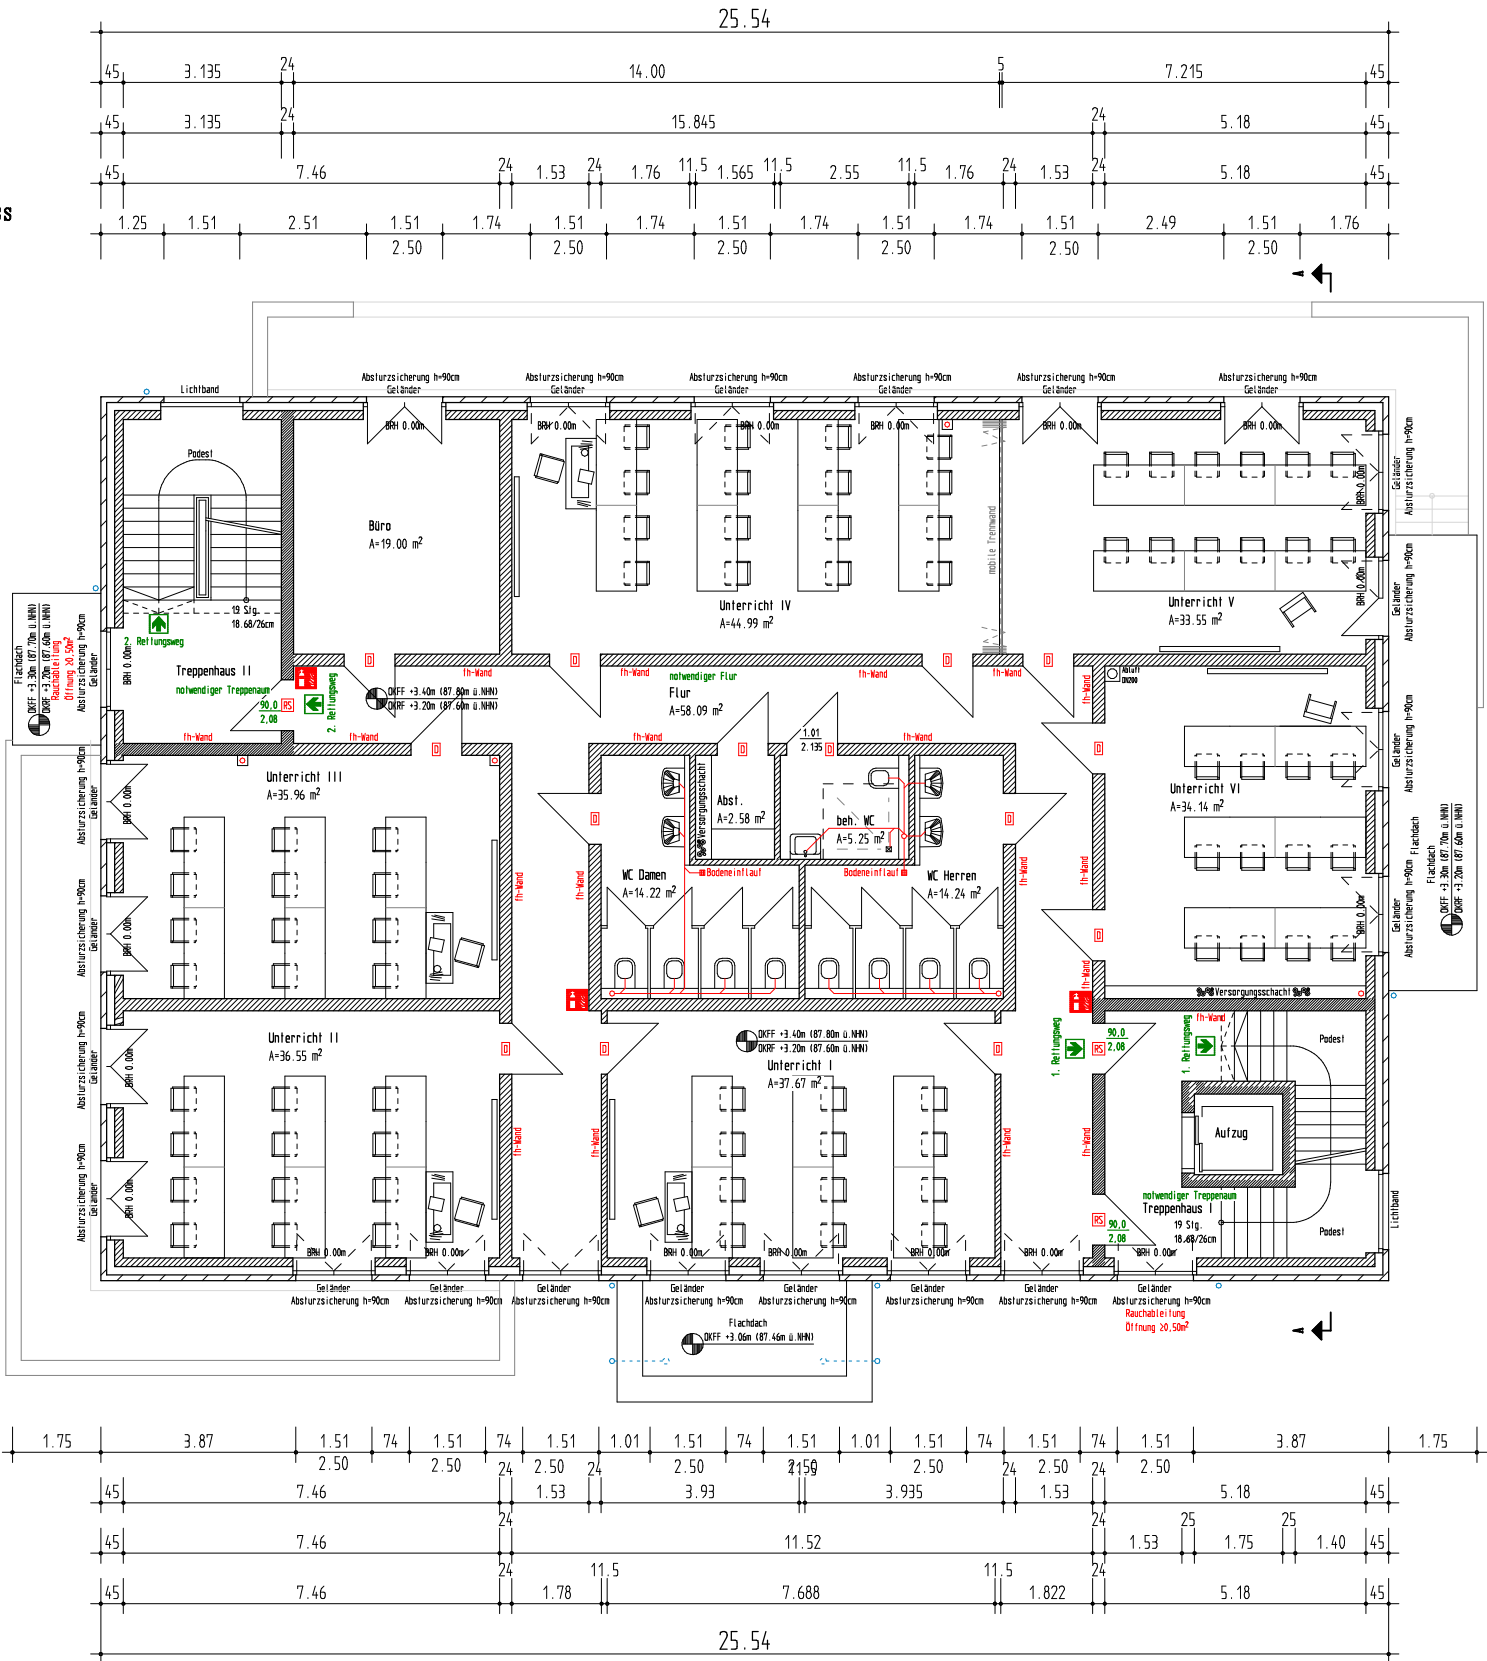

bauaufsichtliche Sichtvermerke:

- Legende
- WM 20-2,0/MG III
 - Mauerwerk (Neu) PP 2-0,35/Db
 - Mauerwerk (Neu) KS 12-1,4/MG Ila
 - Mauerwerk (Neu) KS 20-2,2/MG Ila
 - Stahlbeton (Neu)
 - Trockenbau (Neu)
 - Bestand
 - Neu
 - Brettsperrholzelemente
 - Abbruch
 - Lade- & Leitungsinfrastruktur (E-Mobilität)
 - rollstuhlgerechte Whg. (gem. DIN 18040-2:2011-09)

Maßstab 1:100 0 100 cm 200 cm 300 cm 400 cm 500 cm

Index	Ergänzung / Änderung	Gez./ Gepr.	Datum

DIESE ZEICHNUNG GILT NUR IN VERBINDUNG MIT DEN STATISCHEN UNTERLAGEN !
ALLE MAßE SIND AM BAU ZU PRÜFEN UND MIT DER BAULEITUNG ABZUSTIMMEN !
DIE ALLEINIGEN URBRECHERECHTE LIEGEN BEIM ENTWURFSVERFASSER !

Entwurfsverfasser:
Dipl. - Ing. Bernd Theismann
Ingenieurbüro für Baukonstruktion
Nordstraße 29 • 59227 Ahlen
Fon 02382/85050 Fax 02382/85051
info@theismannundpartner.de

BAUHERR :
DITIB Ahlen - ULU CAMI
i. V. Herr Ali Koca und Mustafa Terken
Rottmannstr. 62, 59229 Ahlen
59229 Ahlen

BAUVORHABEN :
Errichtung einer Begegnungs- und Kulturstätte
mit Büro und Verwaltung
Rottmannstr. 62, 59229 Ahlen 168/170/177/330/
Gemarkung Ahlen, Flur 26, Flurstück/e 681/799

1. Obergeschoss

DATUM : 06.10.2025
MAßSTAB : 1 : 100
AUFTR - Nr. : 274001
BLATT - Nr. : GE05

Ingenieurkammer-Bau
Nordrhein-Westfalen
Mitglied der Kammer

- Hinweis:
Das Brandschutzkonzept durch das Ingenieurbüro
Genähr Beratende Ingenieure ParIG mbB ist zu beachten!
(Stöckholmer Allee 24, 44269 Dortmund)
- Brandschutz:
- Fh = feuerhemmend F30
 - h1 = hochfeuerhemmend F60
 - Fb = feuerbeständig F90
 - nb = nicht brennbar
 - BW = Brandwand
 - WaBW = Wand anstelle einer Brandwand
 - BBW = Bauart einer Brandwand
 - T30, T60, T90 = Feuerwiderstandsklasse
 - M = mechanische Beanspruchung
 - RS = Rauchschutzabschluss (DIN18095)
 - S = Selbstschließend
 - D = Dichtschießend
 - V = Vollwandig
 - N = Nichtabsperribar
 - PS = Panikschloss
 - 1. Rettungsweg
 - 2. Rettungsweg
 - Notausstieg (2. RW)
 - Tür-Öffnungsmaße (roh)
 - Tür-Öffnungsmaße (fertig)
 - Barrierefreiheit (Höhe von DKFFB)