
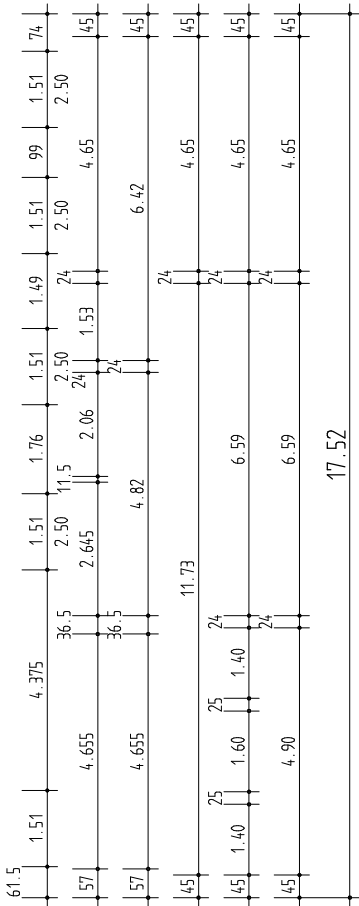
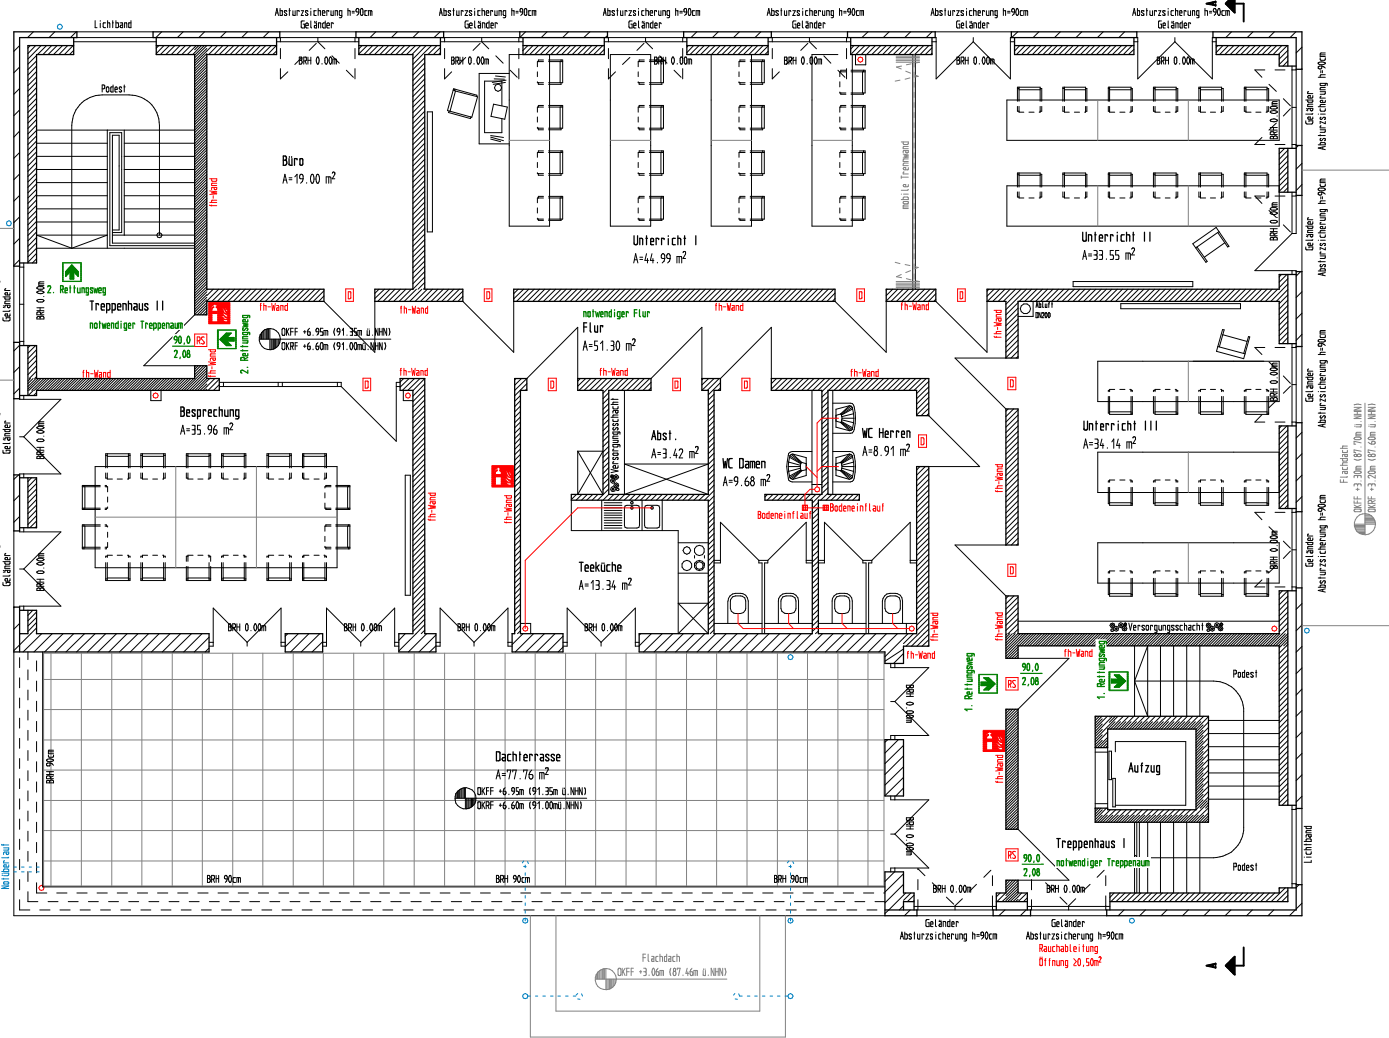
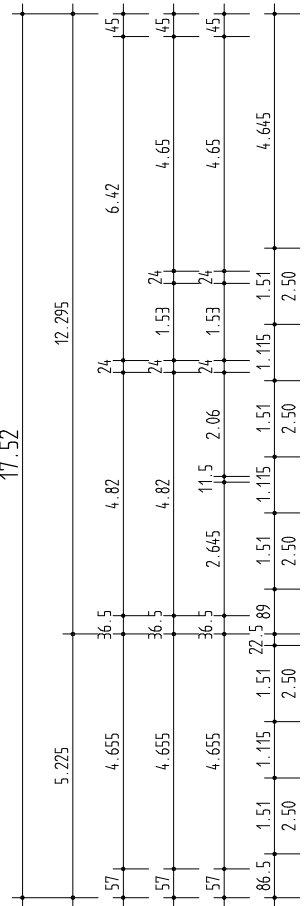


Hinweis Barrierefreiheit:
Das Barrierefrei-Konzept durch das Ingenieurbüro Theismann und Partner,
Dipl.-Ing. Bernd Theismann, ist zu beachten und umzusetzen!
(Nordstraße 29, 59227 Ahlen)

2. Obergeschoss

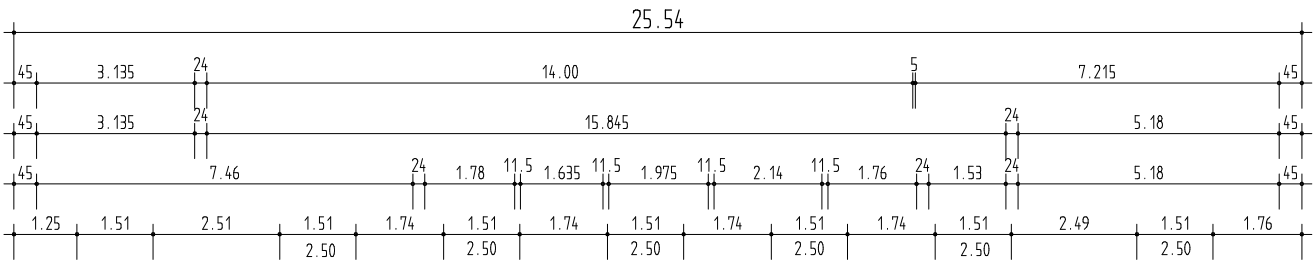

bauaufsichtliche Sichtvermerke:

- Legende
- VMZ 20-2.0/MG III
 - Mauerwerk (Neu) PP 2-0,35/Db
 - Mauerwerk (Neu) KS 12-1,4/MG IIa
 - Mauerwerk (Neu) KS 20-2,2/MG IIa
 - Stahlbeton (Neu)
 - Trockenbau (Neu)
 - Bestand
 - Neu
 - Brettsperreholzelemente
 - Abbruch
 - Lade- & Leitungsinfrastruktur (E-Mobilität)
 - rollstuhlgerechte Whg. (gem. DIN 18040-2:2011-09)

Maßstab 1:100 0 100 cm 200 cm 300 cm 400 cm 500 cm

Index	Ergänzung / Änderung	Gez./Gepr.	Datum

DIESSE ZEICHNUNG GILT NUR IN VERBINDUNG MIT DEN STATISCHEN UNTERLAGEN!
ALLE MAßE SIND AM BAU ZU PRÜFEN UND MIT DER BAULEITUNG ABZUSTIMMEN!
DIE ALLEINIGEN VERBESSERUNGSRECHTE LIEGEN BEIM ENTWURFSVERFASSER!

Entwurfsverfasser:
Dipl. - Ing. Bernd Theismann
Ingenieurbüro für Baukonstruktion
Nordstraße 29 • 59227 Ahlen
Fon 02382/85050 Fax 02382/85051
info@theismannundpartner.de

BAUHERR:
DITIB Ahlen - ULU CAMI
i. V. Herr Ali Koca und Mustafa Terken
Rottmannstr. 82
59229 Ahlen

BAUVORHABEN:
Errichtung einer Begegnungs- und Kulturstätte
mit Büro und Verwaltung
Rottmannstr. 62, 59229 Ahlen
Gemarkung Ahlen, Flur 26, Flurstück/e 168/170/171/330/681/799

2. Obergeschoss

DATUM: 06.10.2025
MAßSTAB: 1 : 100
AUFTR - Nr.: 274001
BLATT - Nr.: GEO6

Ingenieurkammer-Bau
Nordrhein-Westfalen
Mitglied der Kammer
Unterschrift Bauherr
Unterschrift Entwurfsverfasser

- Hinweis:
Das Brandschutzkonzept durch das Ingenieurbüro
Genähr Beralende Ingenieure ParIG mbB ist zu beachten!
(Stückholmer Allee 24, 44269 Dortmund)
- Brandschutz:
- fh = Feuerhemmend F30
 - hf = hochfeuerhemmend F60
 - fb = feuerbeständig F90
 - nb = nicht brennbar
 - BW = Brandwand
 - WaBW = Wand anstelle einer Brandwand
 - BBW = Bauwerk einer Brandwand
 - T30, T60, T90 = Feuerwiderstandsklasse
 - M = mechanische Beanspruchung
 - RS = Rauchschulzabschlus (DIN18095)
 - S = Selbstschließend
 - D = Dichtschließend
 - V = Vollwandig
 - N = Nichtabsperrend
 - PS = Panikschloss
 - 1.01 = Tür-Öffnungsmaße (roh)
 - 2.135 = (Rohbau, Höhe von DKFFB)
 - 90.0 = Tür-Öffnungsmaße (fertig)
 - 2.08 = Barrierefreiheit (Höhe von DKFFB)

