

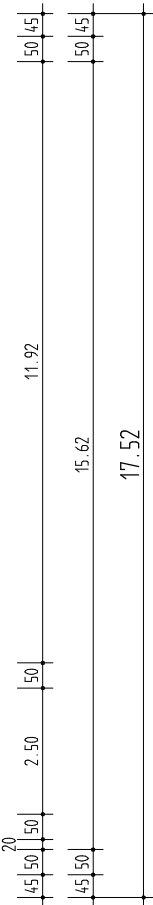
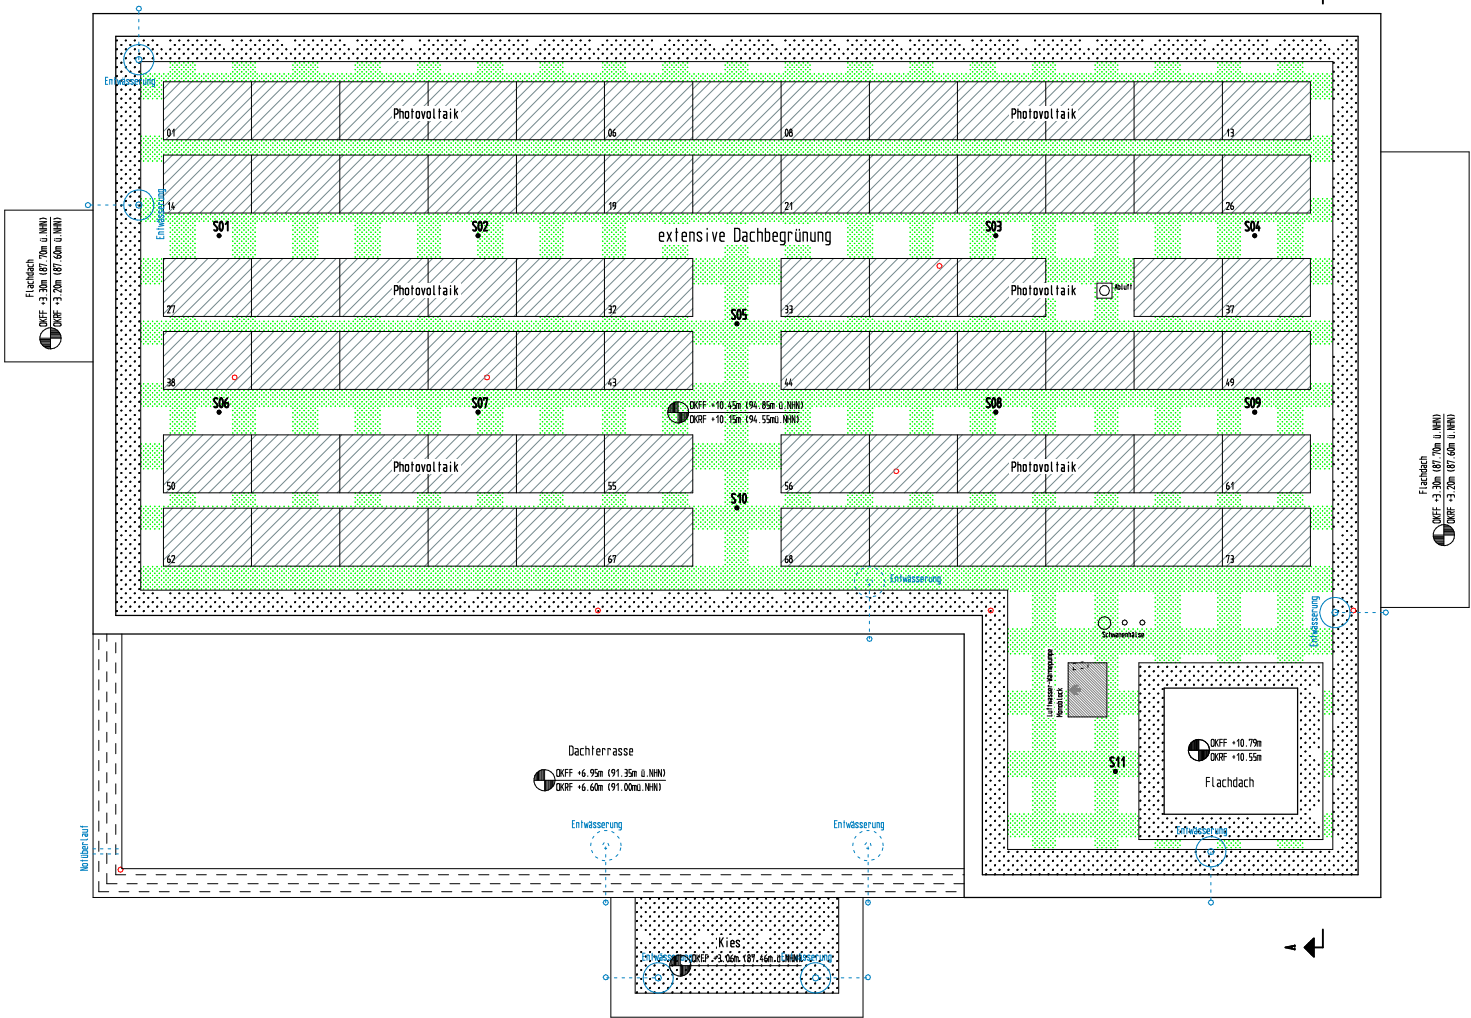


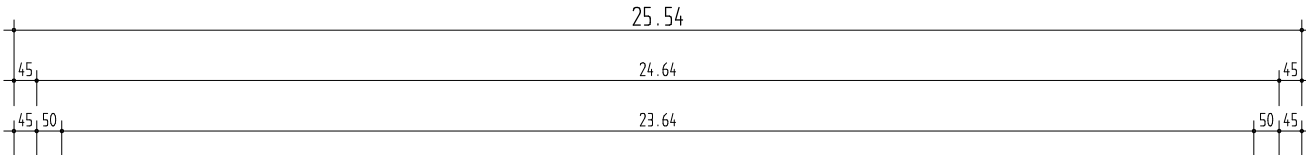

Draufsicht

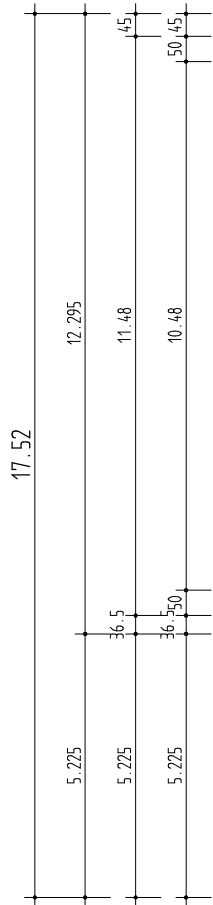

Hinweis Barrierefreiheit:
Das Barrierefrei-Konzept durch das Ingenieurbüro Theismann und Partner,
Dipl.-Ing. Bernd Theismann, ist zu beachten und umzusetzen!
(Nordstraße 29, 59227 Ahlen)

Legende Flachdach

- Kies
- Photovoltaik-Anlage (28kWp)
- Altika (Aluminium)
- Extensive Dachbegrünung h=12cm
- Sekuranten S01 - S12

bauaufsichtliche Sichtvermerke:

Legende

- VMZ 20-2,0/MG III
- Mauerwerk (Neu) PP 2-0,35/Db
- Mauerwerk (Neu) KS 12-1,4/MG IIa
- Mauerwerk (Neu) KS 20-2,2/MG IIa
- Stahlbeton (Neu)
- Trockenbau (Neu)
- Bestand
- Neu
- Brettsperreholzelemente
- Abbruch
- Lade- & Leitungsinfrastruktur (E-Mobilität)
- rollstuhlgerechte Whg. (gem. DIN 18040-2:2011-09)

Maßstab 1:100 0 100 cm 200 cm 300 cm 400 cm 500 cm

Index	Ergänzung / Änderung	Gez./Gepr.	Datum

DIESE ZEICHNUNG GILT NUR IN VERBINDUNG MIT DEN STATISCHEN UNTERLAGEN !
ALLE WERKE SIND AM BAU ZU PRÜFEN UND MIT DER BAULEITUNG ABZUSTIMMEN !
DIE ALLEINIGEN URHEBERRECHTE LIEGEN BEIM ENTWURFSVERFASSER !

Entwurfsverfasser:

Dipl. - Ing. Bernd Theismann
Ingenieurbüro für Baukonstruktion
Nordstraße 29 • 59227 Ahlen
Fon 02382/85050 Fax 02382/85051
info@theismannundpartner.de

BAUHERR :
DITIB Ahlen – ULU CAMI
i. V. Herr Ali Koca und Mustafa Terken
Rottmannstr. 62, 59229 Ahlen
59229 Ahlen

BAUVORHABEN :
Errichtung einer Begegnungs- und Kulturstätte
mit Büro und Verwaltung
Rottmannstr. 62, 59229 Ahlen
Gemarkung Ahlen, Flur 26, Flurstück/e 168/170/177/330/
681/799

Datum	06.10.2025
Maßstab	1 : 100
AUPT - Nr.	274001
BLATT - Nr.	GE07

Ingenieurkammer-Bau
Nordrhein-Westfalen
Mitglied der Kammer


Photovoltaik (min. 30% der Dach-Grundfläche):
Dach-Grundfläche: ca. 480,48m²
481,00 m² x 30% = 144,30m² ; 2,01m² = 71,79 Stück-72 Stück
(1x Modul = 1,15m x 1,75m = 2,01m²)
min. 72 Module erf. => 73 Module vorh.

Hinweis:


Das Brandschutzkonzept durch das Prüflingenieurbüro
Genähr Beratende Ingenieure ParIG mbH ist zu beachten!
(Stöckholmer Allee 24, 44269 Dortmund)

Brandschutz:

- fh = feuerhemmend F30
- hf = hochfeuerhemmend F60
- fb = feuerbeständig F90
- nb = nicht brennbar
- BW = Brandwand
- WaBW = Wand anstelle einer Brandwand
- BBW = Bauart einer Brandwand
- T30, T60, T90 = Feuerwiderstandsklasse
- M = mechanische Beanspruchung
- RS = Rauchschulzabschluss (DIN18095)
- S = Selbstschließend
- D = Dichtschließend
- V = Vollwandig
- N = Nichtabsperren
- PS = Panikschloss

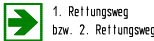

1. Rettungsweg
bzw. 2. Rettungsweg

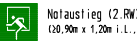

Notausstieg (2.RW)
(20,90m x 1,20m i.L., 80h st.20m)
2.06 Barrierefreiheit (Höhe von OKFFB)

1.81
2.135
Tür-Öffnungsmaße (roh)
(Rohbau, Höhe von OKFFB)

90.0
2.06
Tür-Öffnungsmaße (fertig),
Barrierefreiheit (Höhe von OKFFB)

Detail Solar-Gründach (FA. Optigrün)

M 1:25

